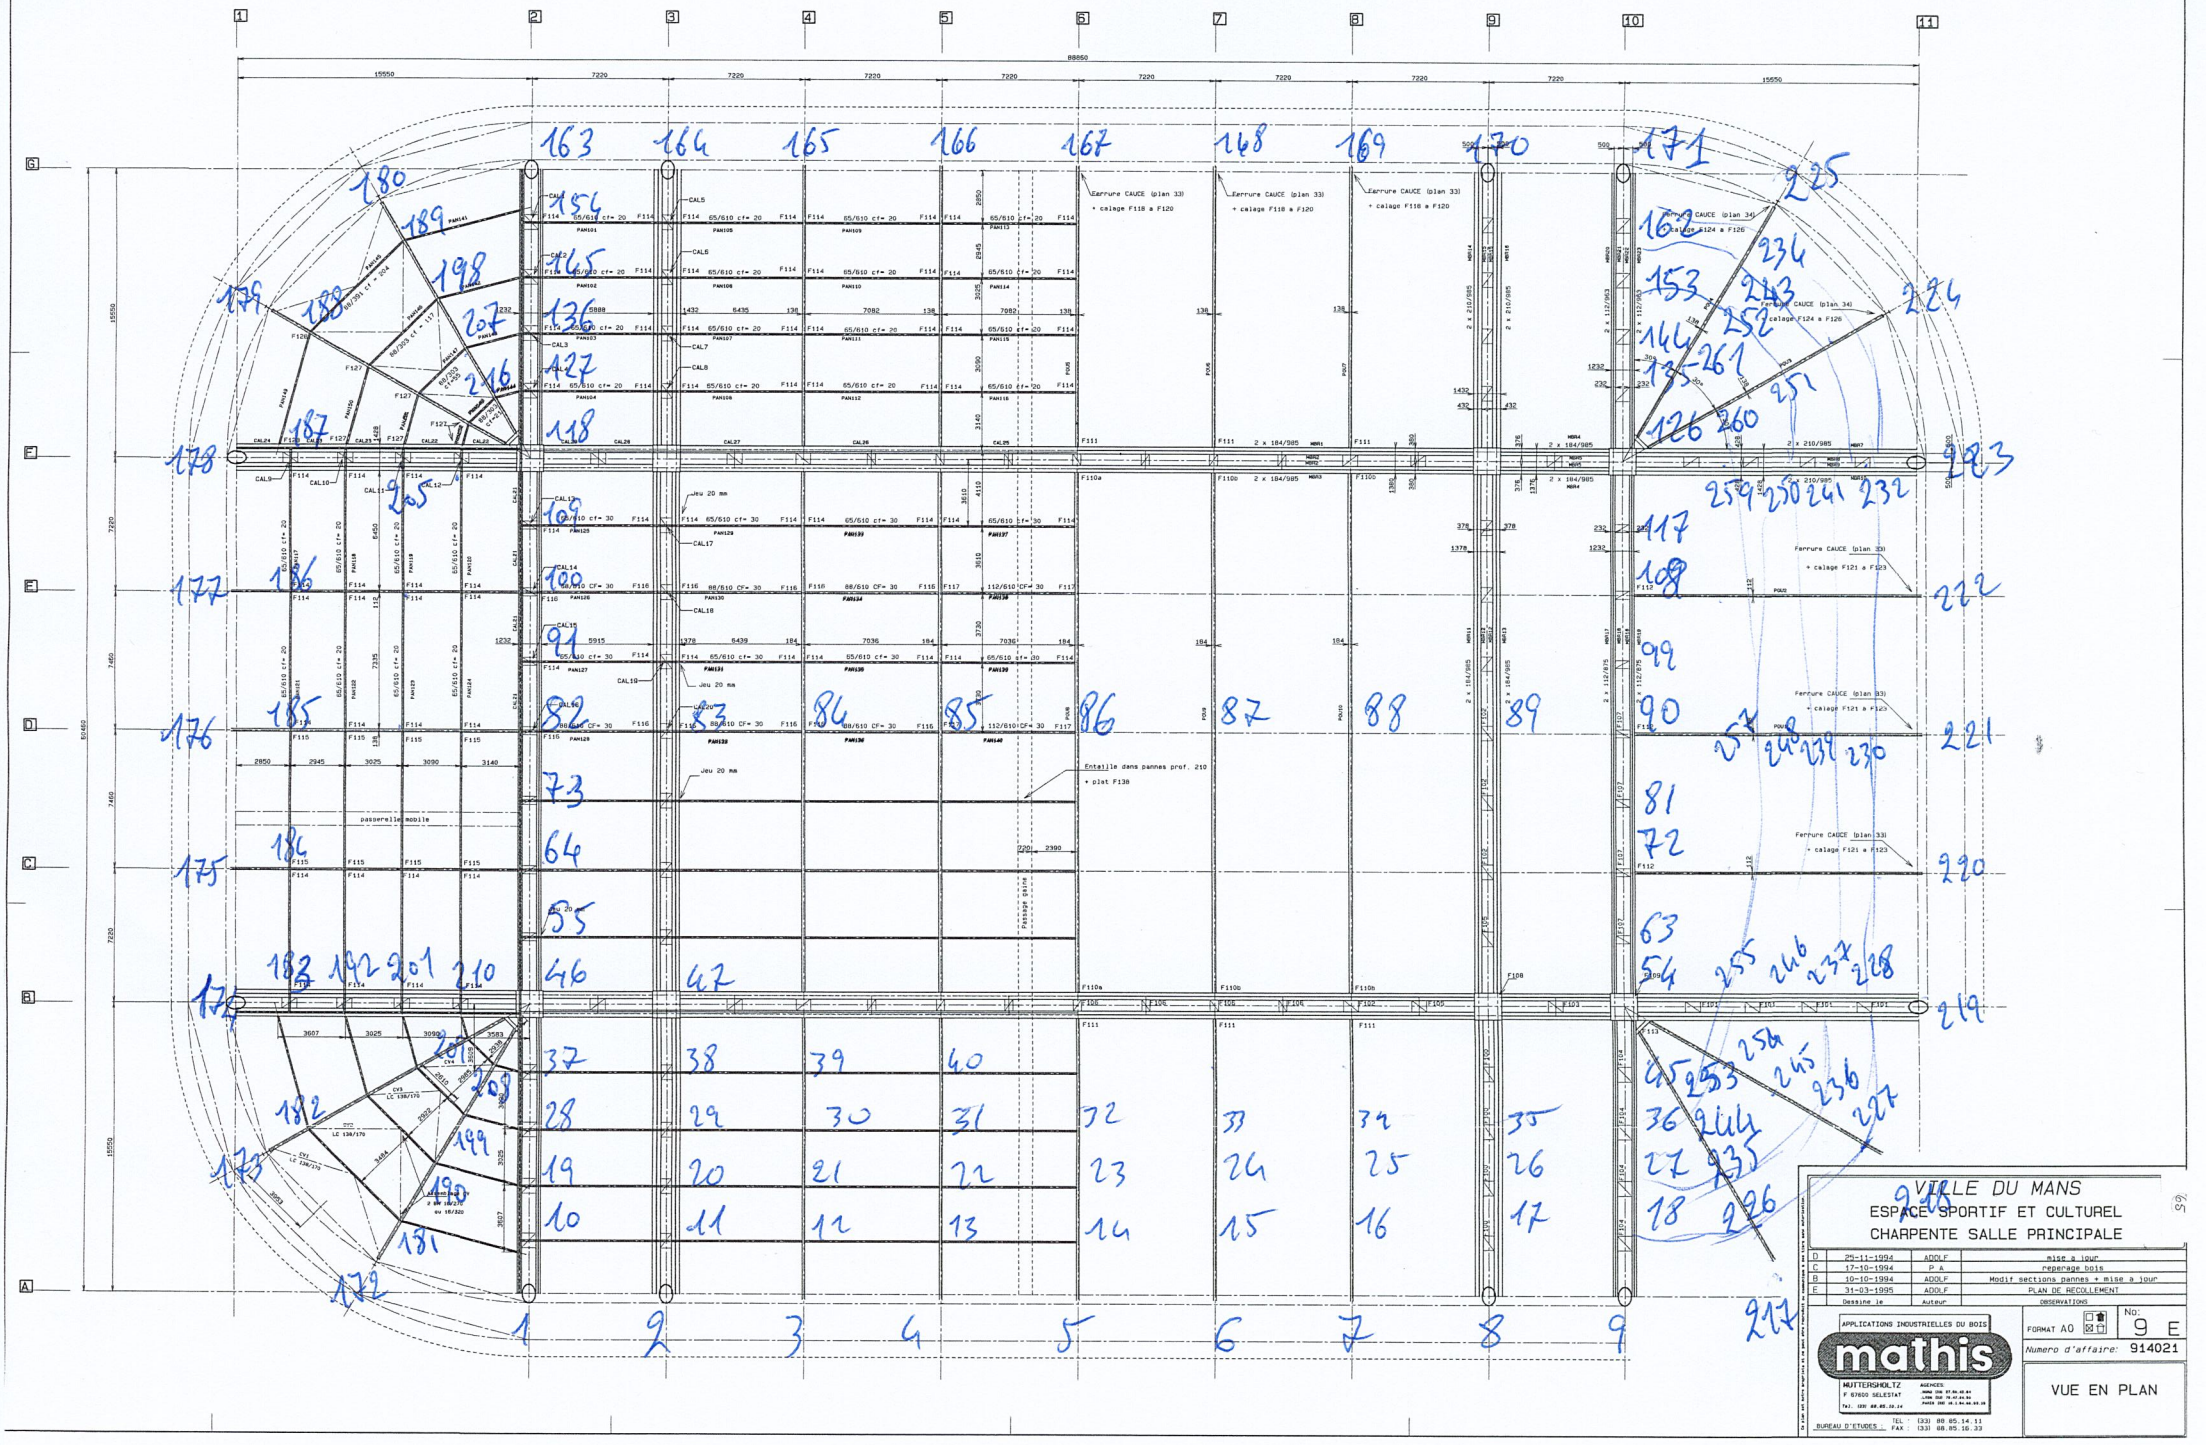

VILLE DU MANS
ESPACE SPORTIF ET CULTUREL
CHARPENTE SALLE PRINCIPALE
D 25-11-1994 ADOLF mise a jour
C 17-10-1994 P A repenage bois
B 10-10-1994 ADOLF Modif sections pannes + mise a jour
E 31-03-1995 ADOLF PLAN DE RECOLLEMENT
Dessine le Auteur OBSERVATIONS
APPLICATIONS INDUSTRIELLES DU BOIS
mathis
MUTTERSHOLTZ
F 67600 SELESTAT
BUREAU D'ETUDES
TEL : (33) 88.85.14.11
FAX : (33) 88.85.16.33
FORMAT A0
No: 9 E
Numero d'affaire: 914021
VUE EN PLAN